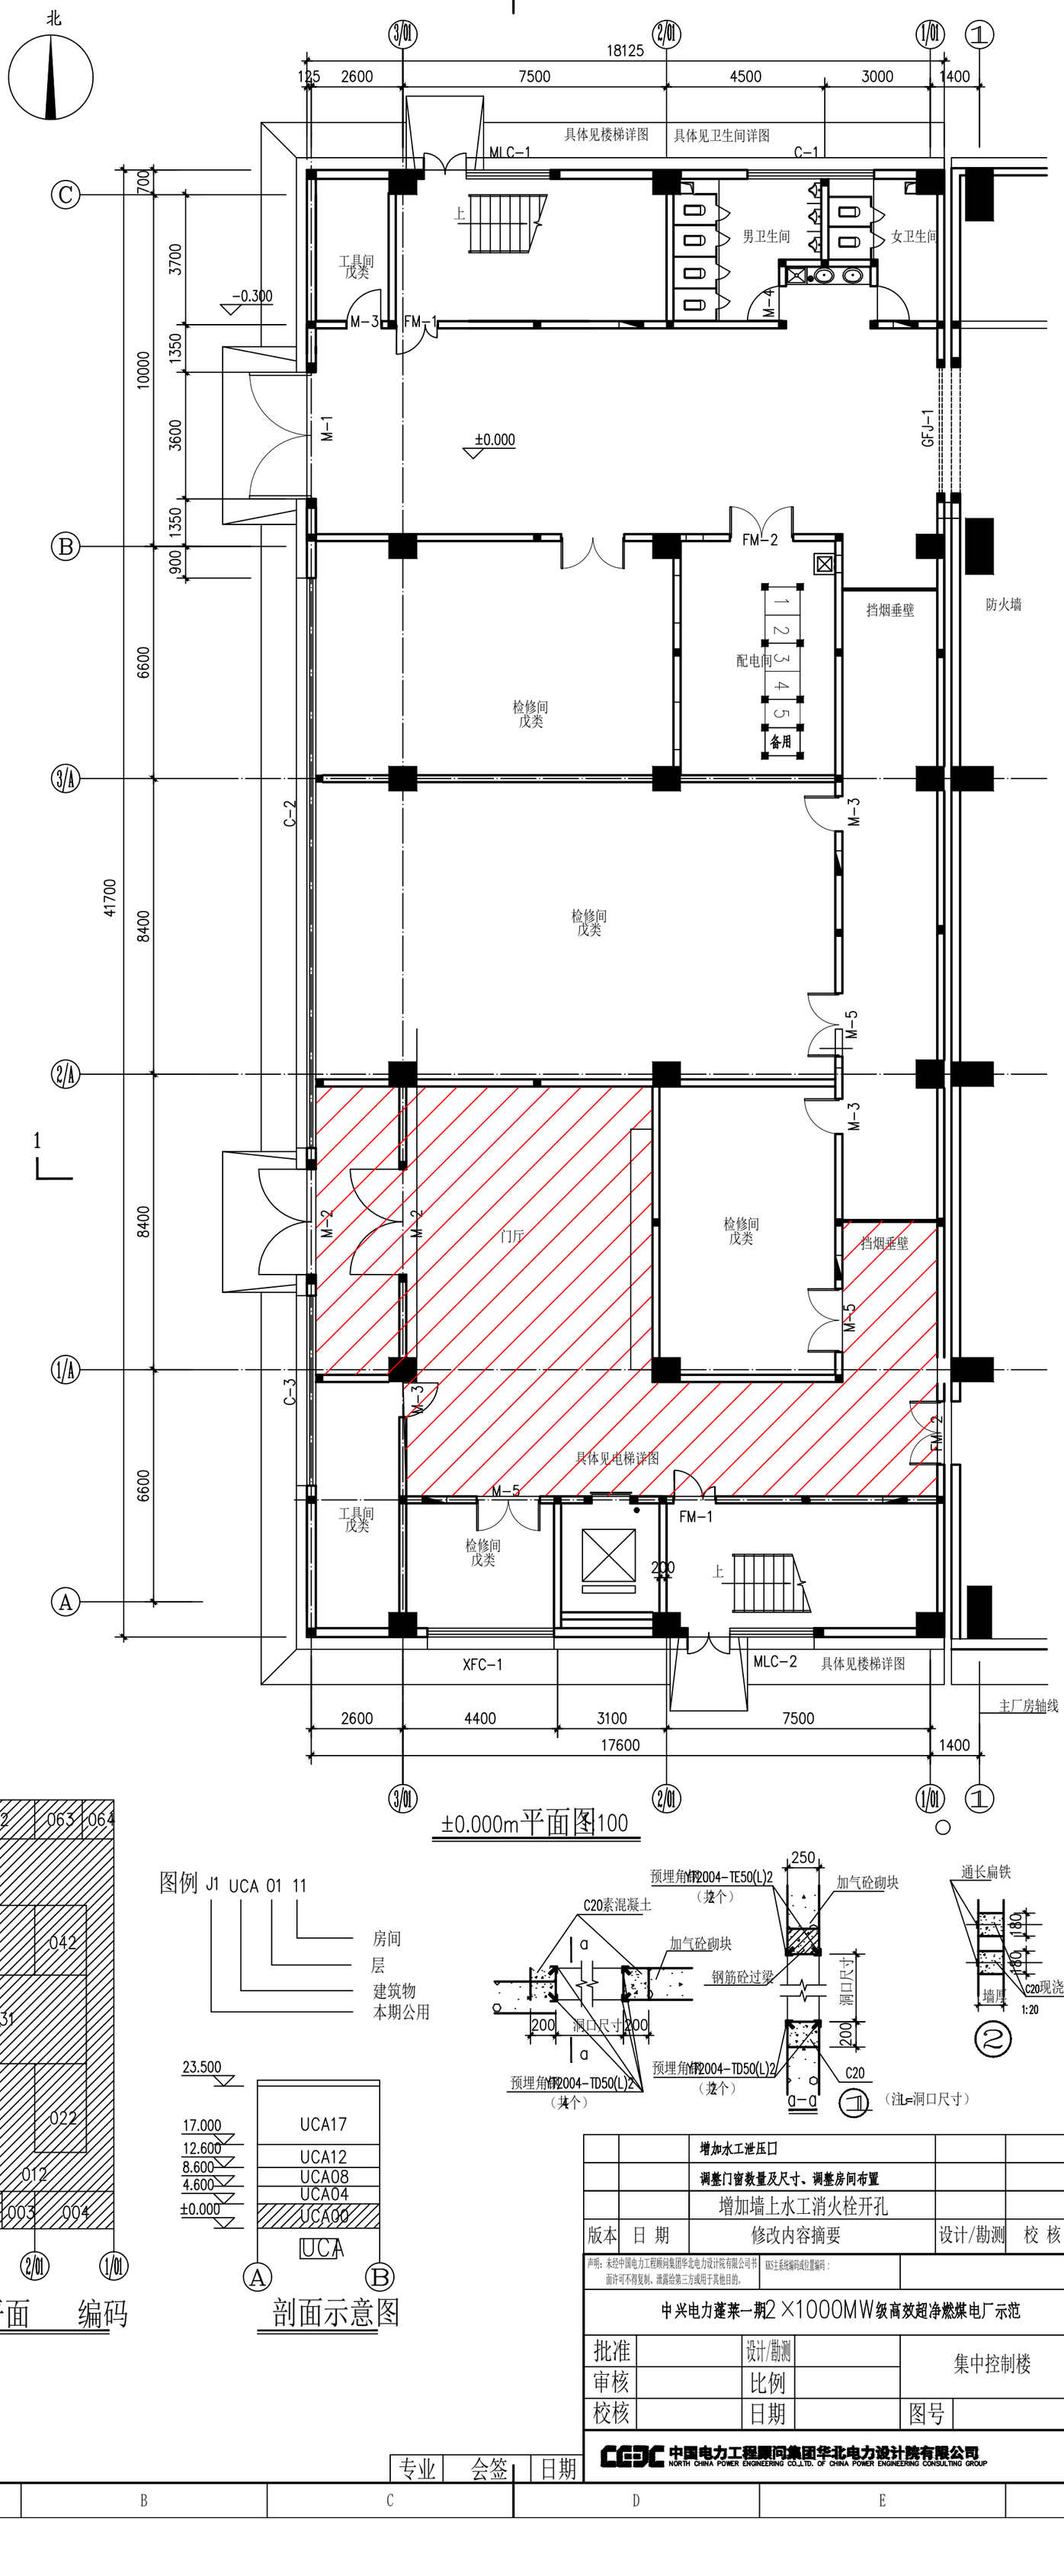


		增加水工泄压口				
		调整门窗数量及尺寸、调整房间布置				
		增加墙上水工消火栓开孔				
版本	日 期	修改内容摘要	设计/勘测	校 核	审 核	批 准

声明：未经中国电力工程顾问集团华北电力设计院有限公司书面许可不得复制、泄露给第三方或用于其他目的。

BIM主系统编码或位置编码：

图纸级别

中兴电力蓬莱一期2×1000MW级高效超净燃煤电厂示范 工程

施工图 设计阶段

批准		设计/勘测		集中控制楼	平面图
审核		比例			
校核		日期		图号	版本

中国电力工程顾问集团华北电力设计院有限公司
NORTH CHINA POWER ENGINEERING CO.,LTD. OF CHINA POWER ENGINEERING CONSULTING GROUP

专业	会签	日期