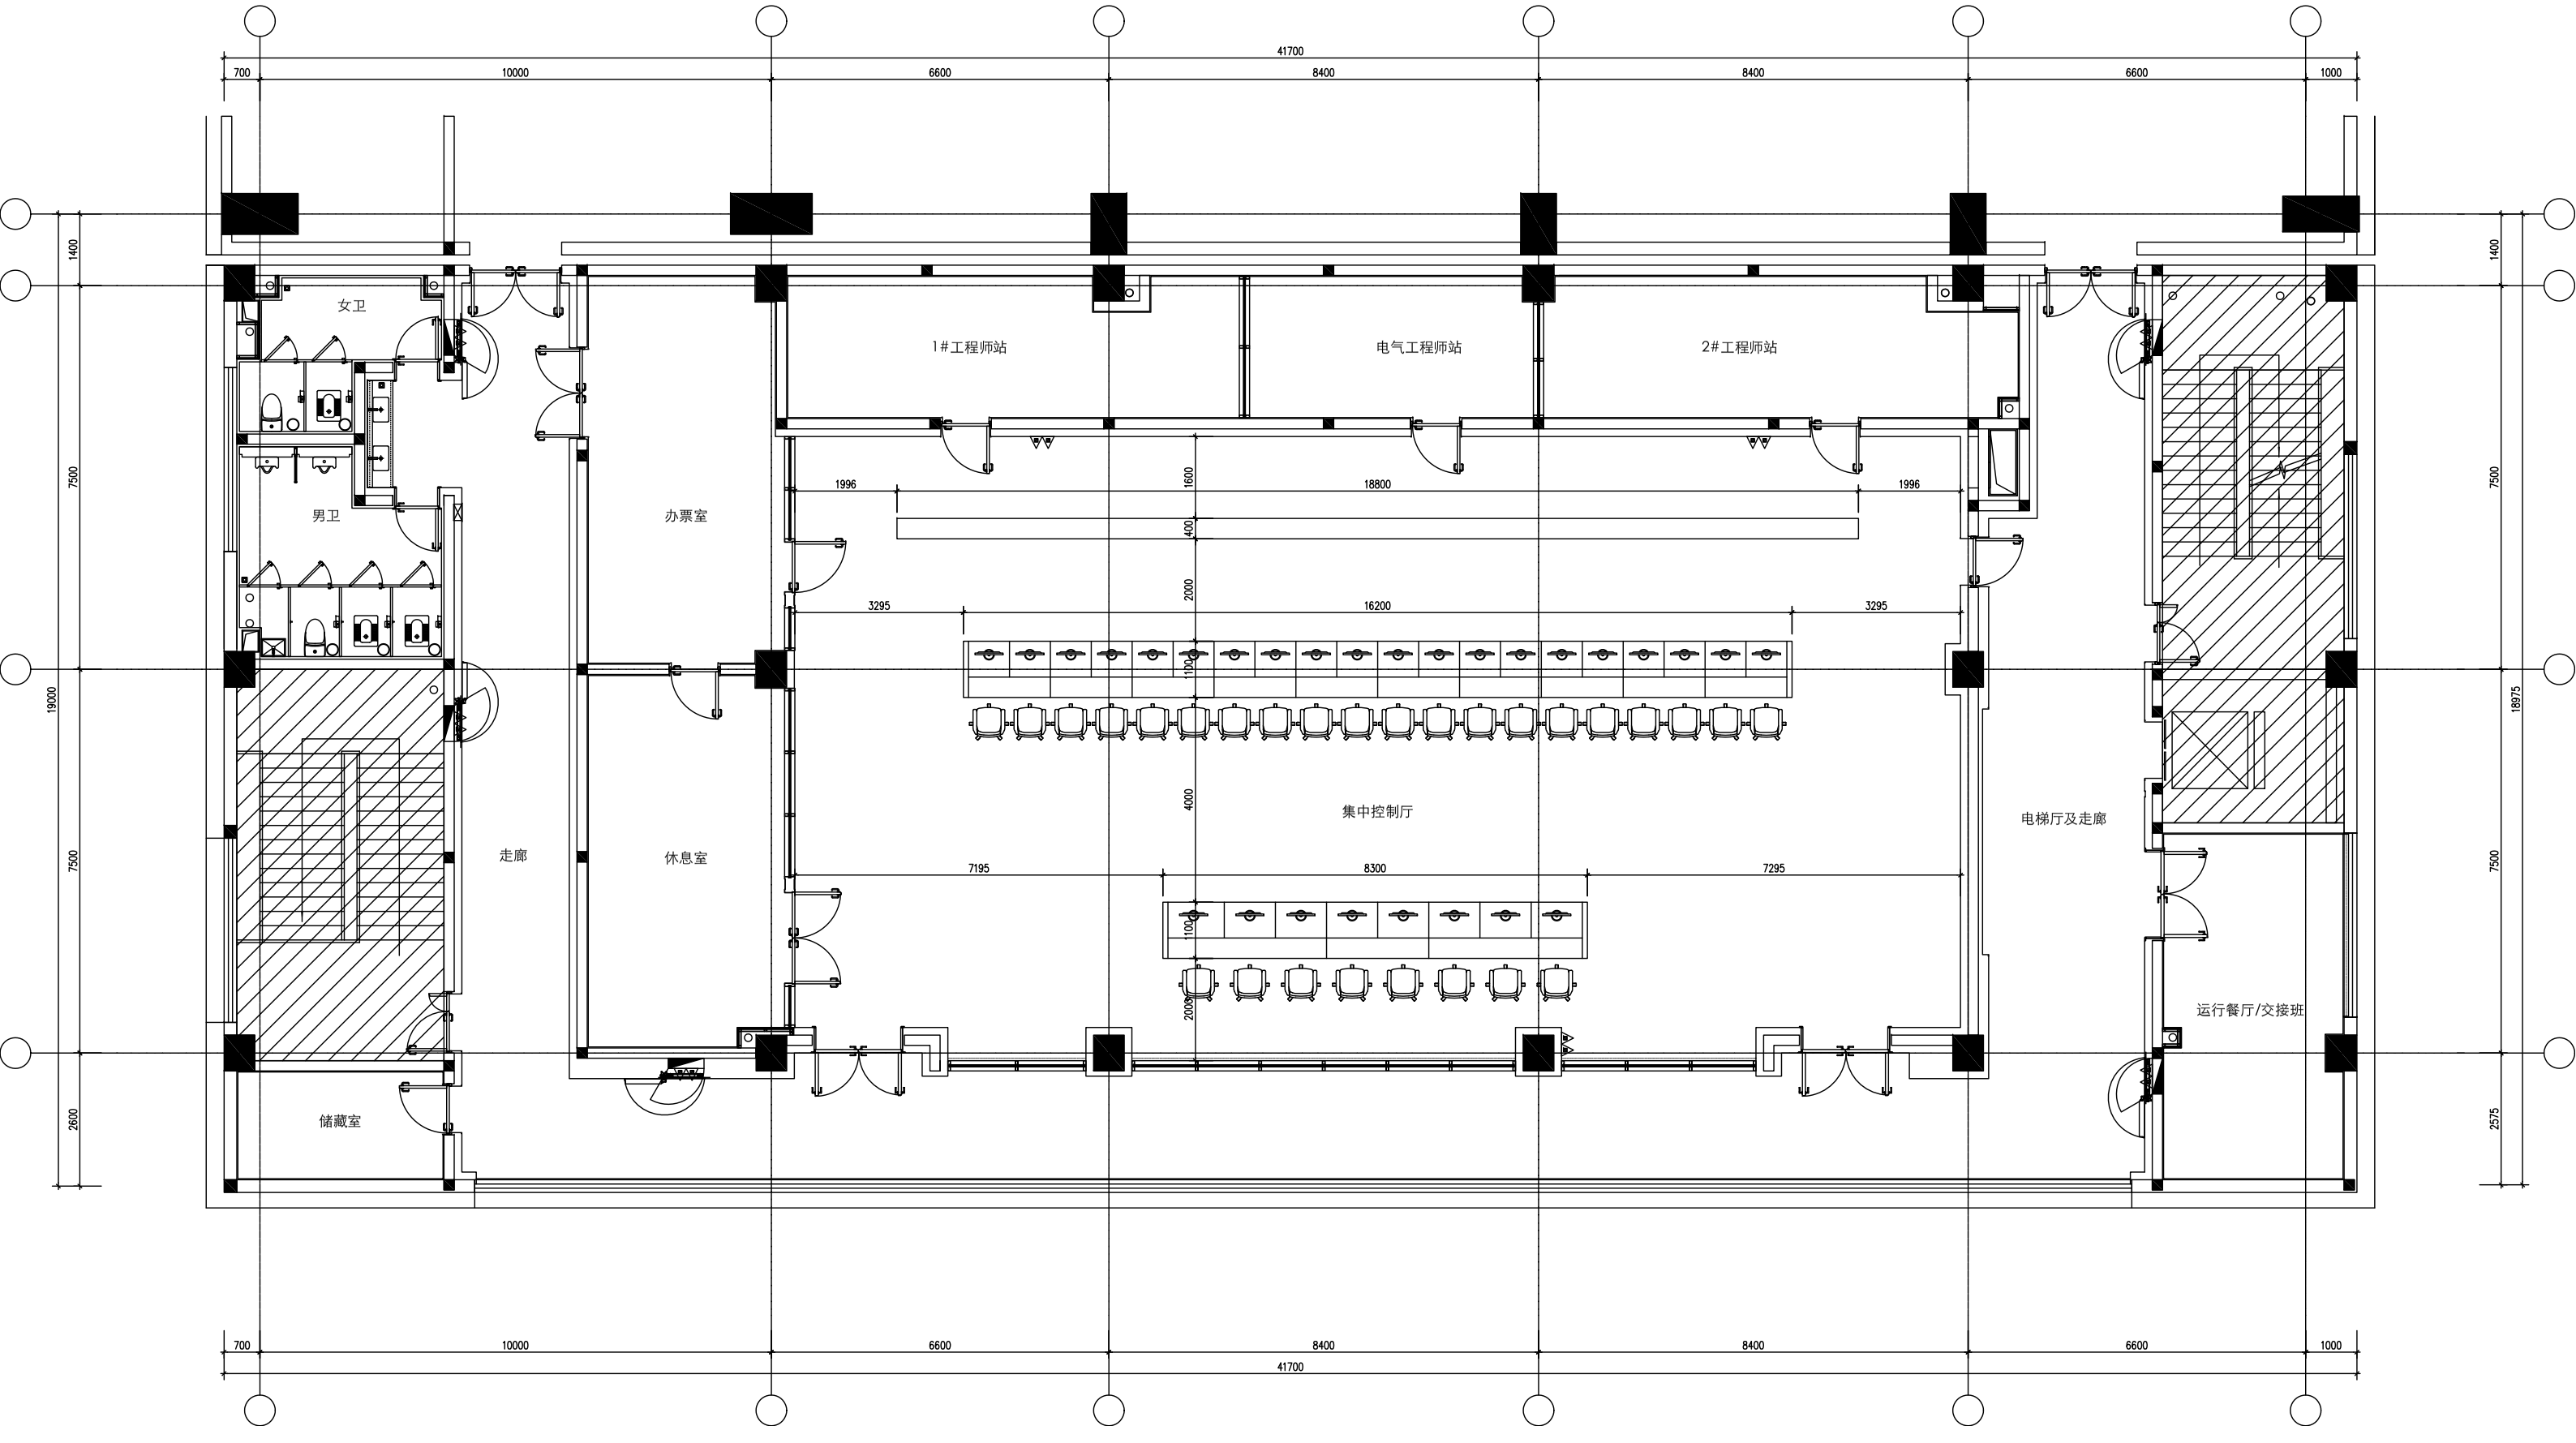

41700
700
10000
6600
8400
8400
6600
1000
1400
7500
19000
2600
女卫
男卫
办票室
1#工程师站
电气工程师站
2#工程师站
1996
18800
1996
1600
400
2000
3295
16200
3295
1100
4000
集中控制厅
7195
8300
7295
1100
2000
走廊
休息室
储藏室
电梯厅及走廊
运行餐厅/交接班
7500
18975
7500
2575
700
10000
6600
8400
8400
6600
1000
41700